
E-401 IPA Feed Vaporizer	R-401 IPA Reactor	H-401 Reactor Furnace	E-402 Reactor Effluent Cooler	V-401 Phase Separator	T-401 Acetone Scrubber	T-402 Acetone Column	E-403 Acetone Column Condenser	E-404 Acetone Column Reboiler	P-401 IPA Feed Pump	D-401 Acetone Reflux Drum

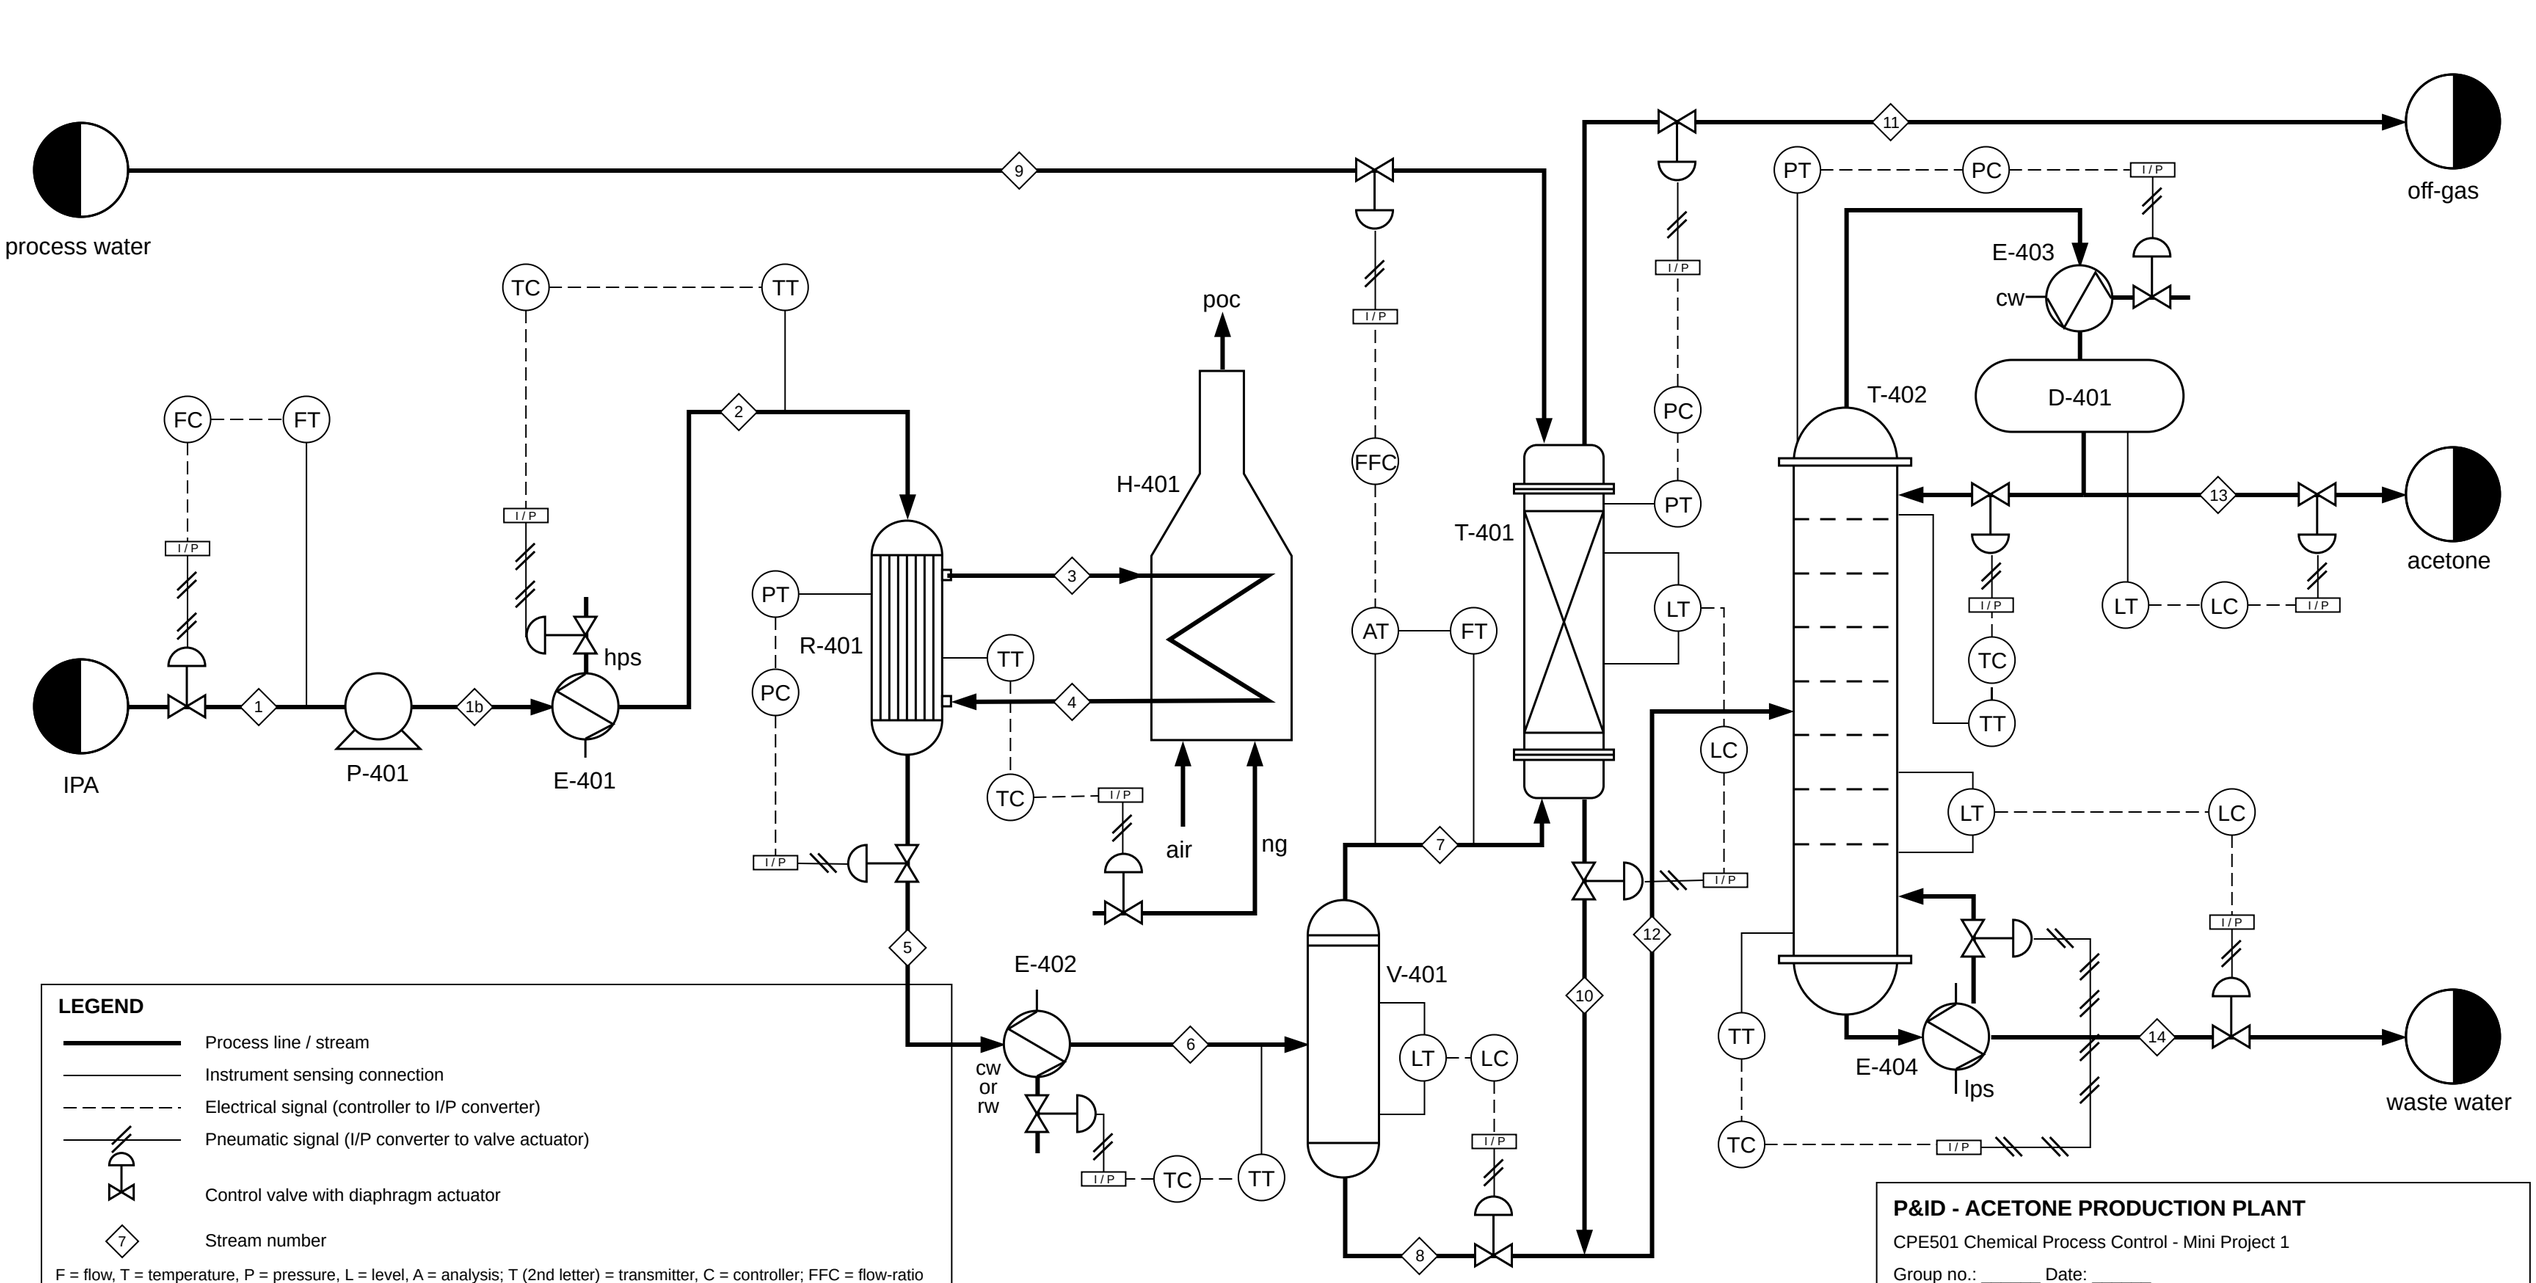

LEGEND

- Process line / stream
- Instrument sensing connection
- Electrical signal (controller to I/P converter)
- Pneumatic signal (I/P converter to valve actuator)
- Control valve with diaphragm actuator
- 7 — Stream number

F = flow, T = temperature, P = pressure, L = level, A = analysis; T (2nd letter) = transmitter, C = controller; FFC = flow-ratio controller; I/P = current-to-pneumatic converter. Utilities: hps / lps = high / low-pressure steam, cw = cooling water, rw = refrigerated water, ng = natural gas, poc = products of combustion.

P&ID - ACETONE PRODUCTION PLANT

CPE501 Chemical Process Control - Mini Project 1

Group no.: _____ Date: _____

Members: _____